KITCHEN ISLAND — CABINET BOX SCHEMATIC

6030 E 11th · 107 5/8" cabinet+opening run · 3 cm stone waterfall BOTH ends (full depth) · Flat-pack: Cab Parts, Grand Junction

1 / DIMENSIONED PLAN (box layout, top view)

Boxes 24" deep · Frameless / European style · approx. 3/4" = 1'-0"

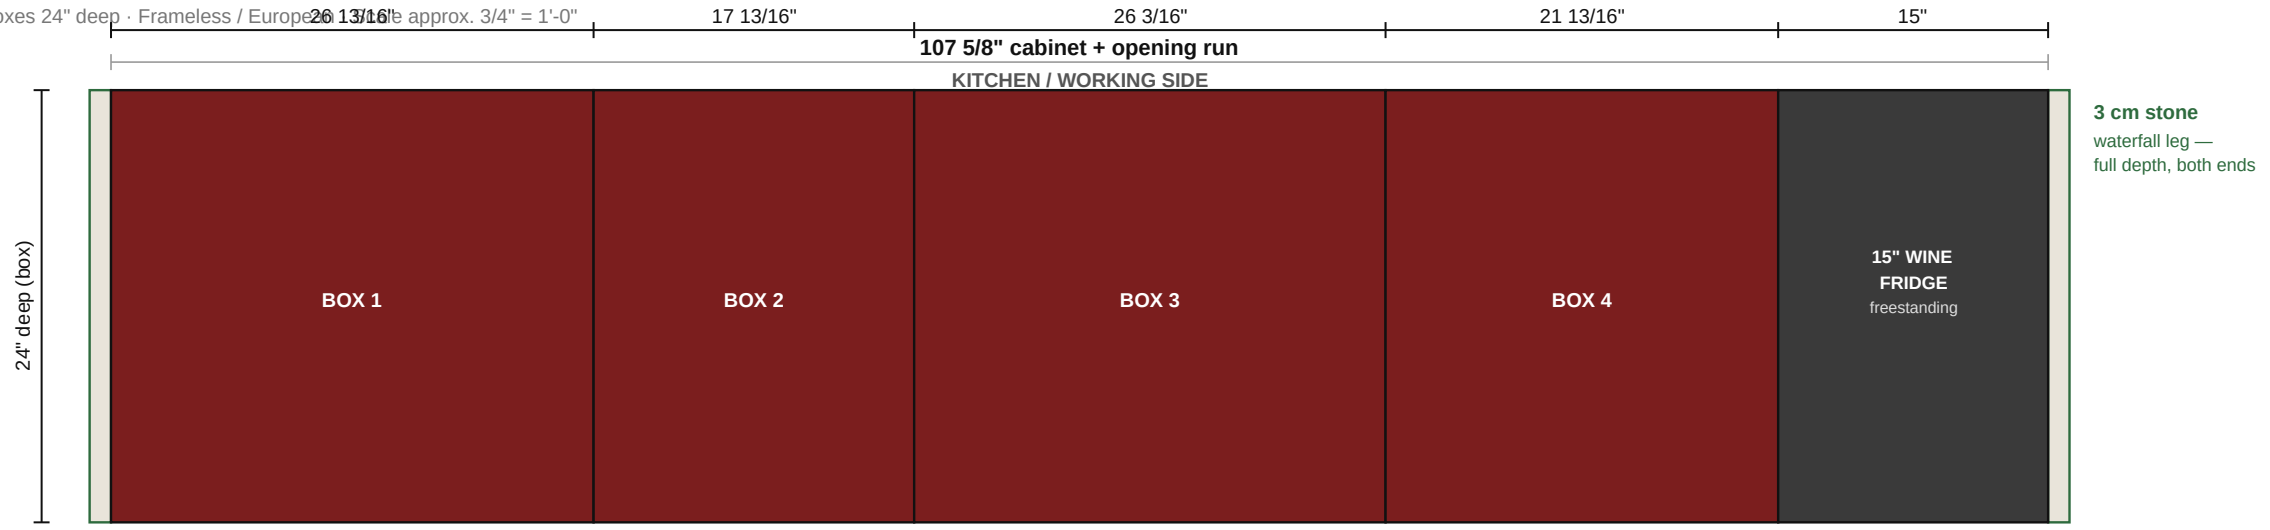

2 / FRONT ELEVATION (island face)

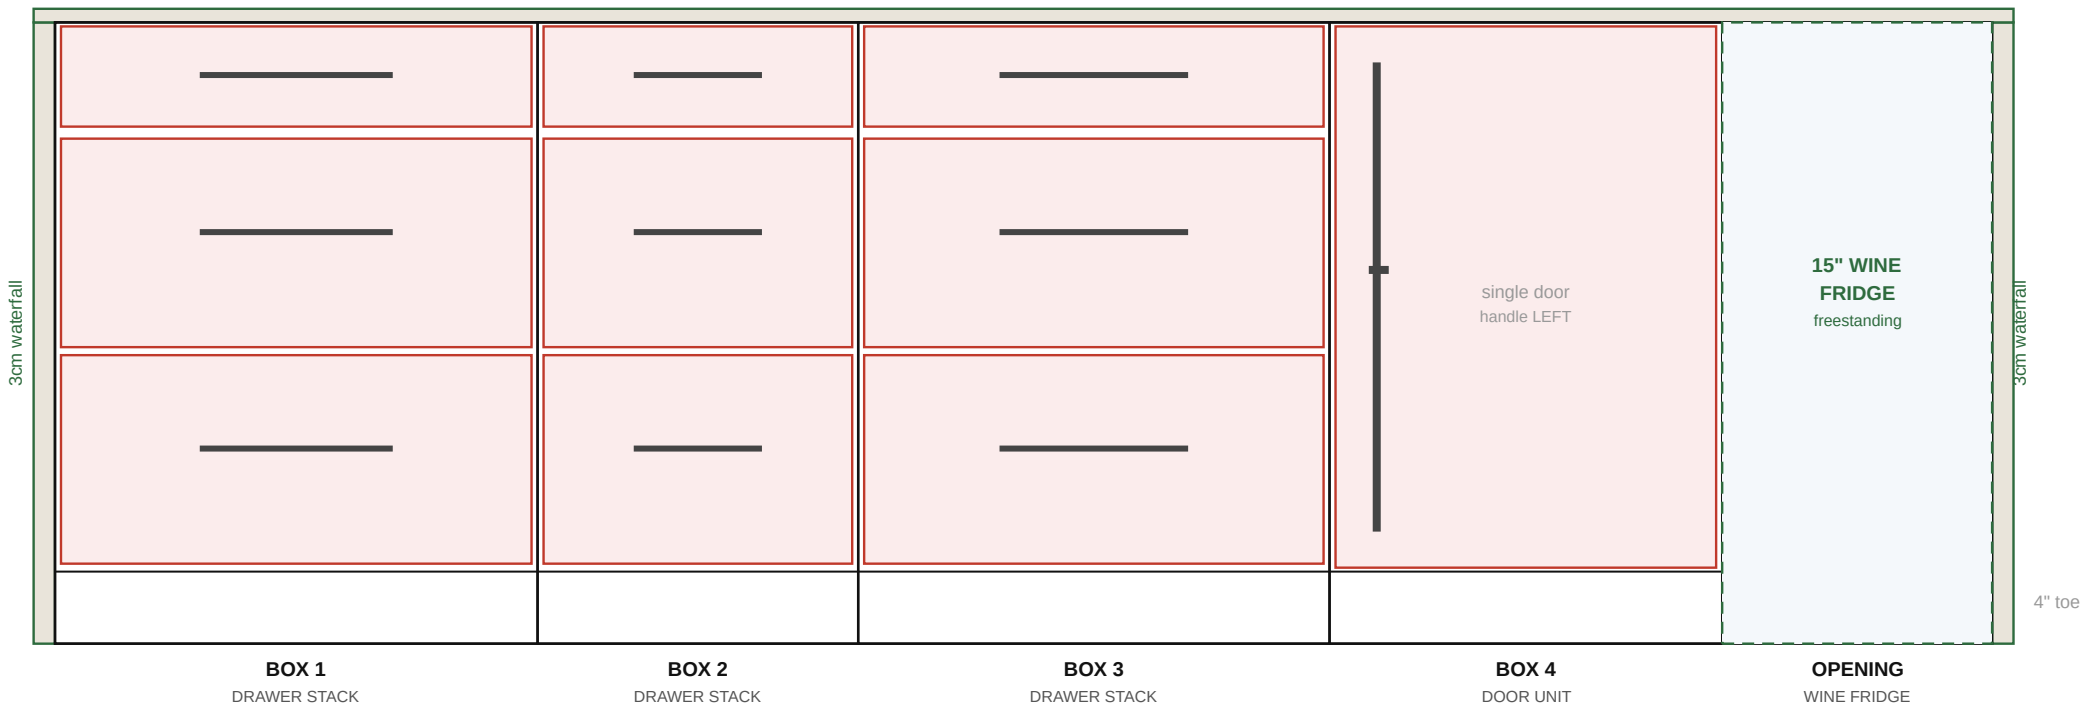

CRITICAL LENGTH CHAIN

107 5/8" run = 26 13/16" + 17 13/16" + 26 3/16" (drawers) + 21 13/16" (door) + 15" (fridge opening).

3 cm stone waterfall on BOTH ends, full 24" depth. If waterfall wraps outside the run, stone overall ≈ 110" (run + 2 × 1 3/16"). Field-verify layout with Arrow Stone.

Cabinet dimension is calculated — NOT a fabrication release. Field-measure existing boxes, confirm the 15" wine-fridge rough opening/ventilation, absorb tolerances in filler/scribe.

Do not reduce the wine-fridge clear opening to force the boxes into the span.

NOTES

1. All dims to finished faces U.N.O.
2. Top + both waterfall ends: 3 cm stone (Lily's selection).
3. Fronts: existing RED LACQUER; HORIZONTAL pulls.
4. Coordinate floor power, camera cords, fridge receptacle & ventilation.
5. Box 4 = SINGLE door, handle LEFT.

BOX SCHEDULE

BOX	TYPE	WIDTH	CONFIG
1	Drawer stack	26 13/16"	3 drwr 6/12/12
2	Drawer stack	17 13/16"	3 drwr 6/12/12
3	Drawer stack	26 3/16"	3 drwr 6/12/12
4	Door unit	21 13/16"	SINGLE door, L pull
—	Wine fridge	15" opening	Freestanding

4 boxes to order (fridge = gap).