KITCHEN ISLAND - PLAN & OVERALL GEOMETRY

108 in x 60 in x 36 in overall | 3 cm Taj Mahal quartzite surface | schematic design set

1 / DIMENSIONED PLAN

Scale: 1/2 in = 1 ft

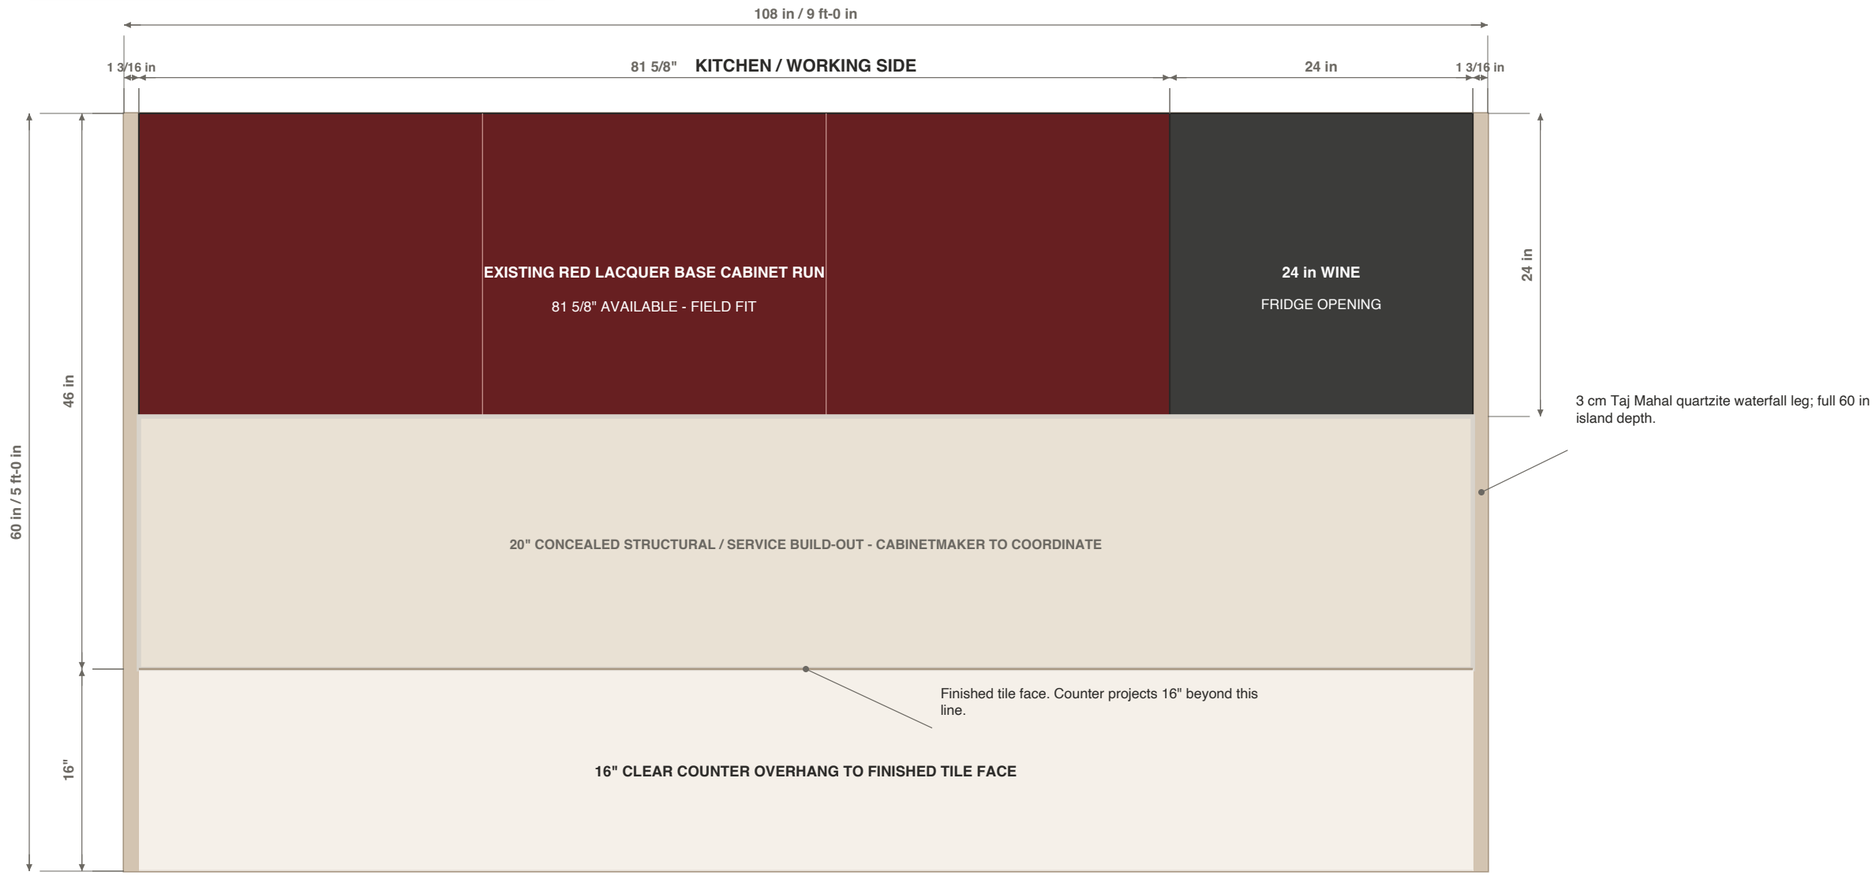

SEATING SIDE

CRITICAL LENGTH CHAIN

108 in overall = 1 3/16 in left waterfall + 81 5/8" cabinet zone + 24 in appliance opening + 1 3/16 in right waterfall.

The cabinet dimension is calculated, not a fabrication release. Field-measure the existing cabinet boxes, confirm appliance rough-opening/ventilation requirements, and absorb tolerances with intentional filler/scribe panels.

Do not reduce the manufacturer's required clear wine-fridge opening to force the existing cabinets into the span.

PLAN NOTES

1. All dimensions are to finished faces unless noted otherwise.
2. Island top and both full-depth waterfall ends: Taj Mahal quartzite, 3 cm actual thickness.
3. Structure terminates 16" behind seating edge; provide concealed steel support sized by fabricator/engineer.
4. Coordinate floor power route, accessible wine-fridge receptacle, service path, and ventilation before closing build-out.

KITCHEN ISLAND - LONG ELEVATIONS

Kitchen-side appliance/cabinet layout and seating-side tile layout

1 / KITCHEN-SIDE ELEVATION

Scale: 1/2 in = 1 ft

Confirm appliance model, rough opening, ventilation and toe-kick grille before fabrication.

2 / SEATING-SIDE ELEVATION

Scale: 1/2 in = 1 ft I tile face recessed 16" in plan

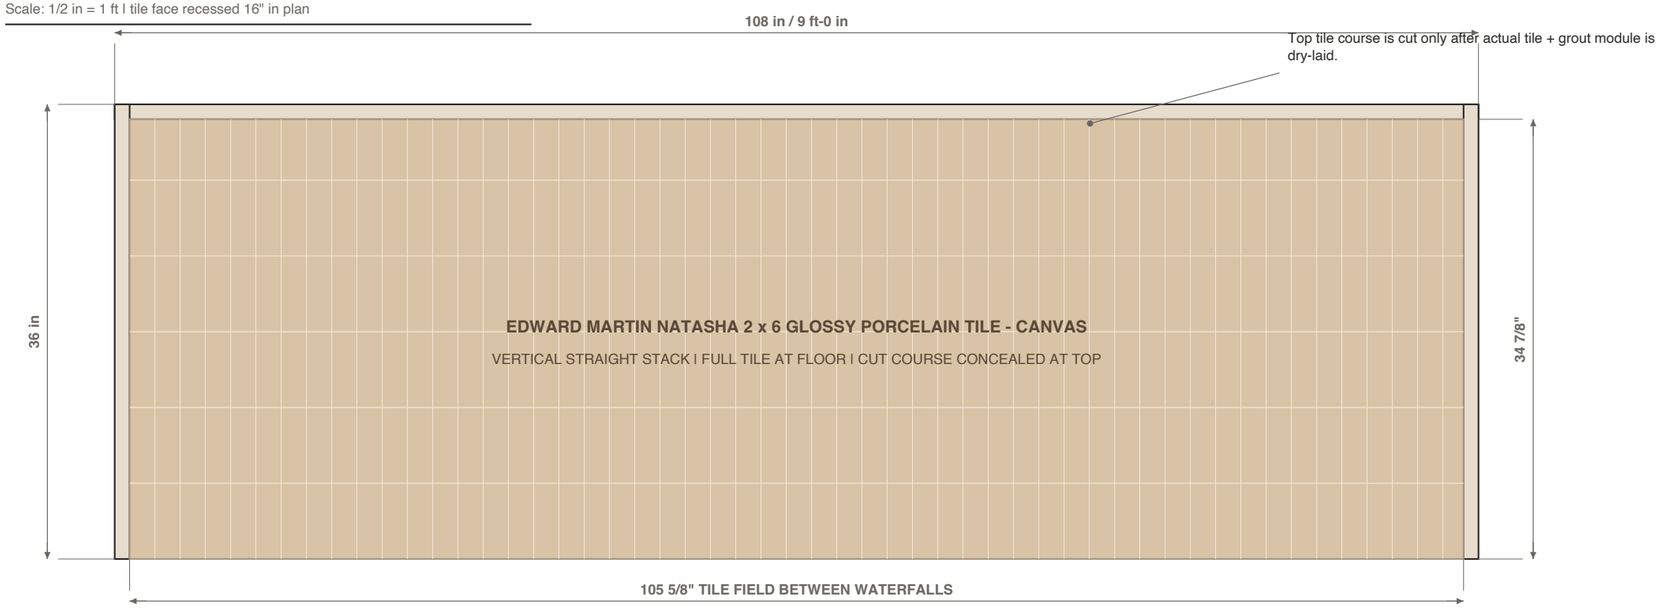

KITCHEN ISLAND - SECTION, END ELEVATION & NOTES

Structural intent, overhang geometry, tile sequencing and material coordination

1 / TRANSVERSE SECTION THROUGH ISLAND

Scale: 1/2 in = 1 ft l section away from waterfall end

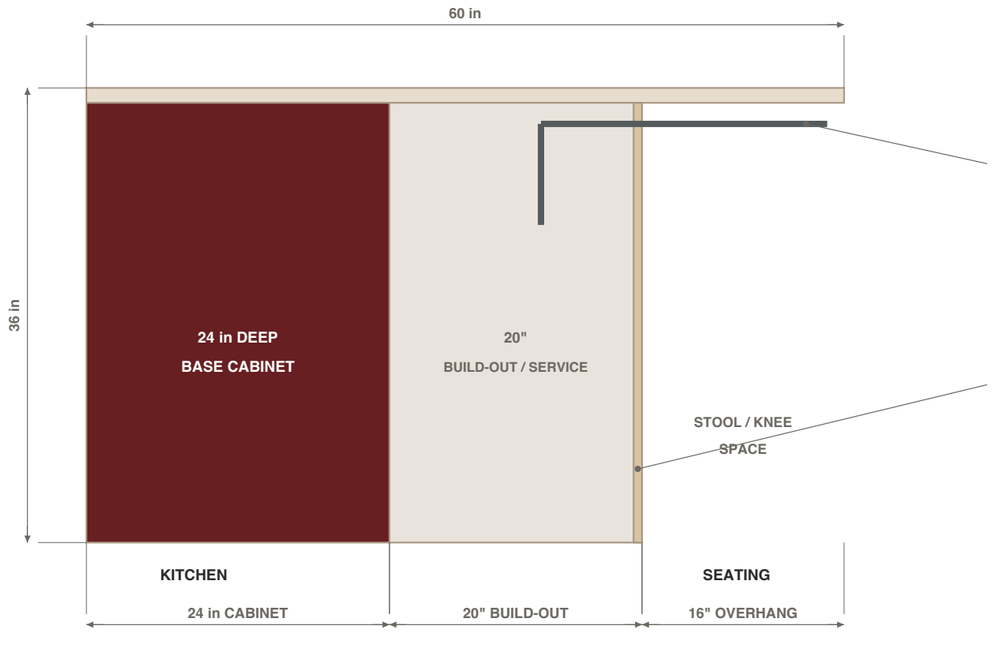

Concealed steel support; fabricator/engineer to size and space. Do not load tile assembly.

Finished tile face establishes the 16" overhang datum.

2 / END ELEVATION

Scale: 1/2 in = 1 ft l both ends identical

Fabricator to submit a scaled slab layout for approval. Prioritize vein continuity from the top across both mitered waterfall returns; final slab selection by designer.

3 / TILE LAYOUT RULE

Not to scale

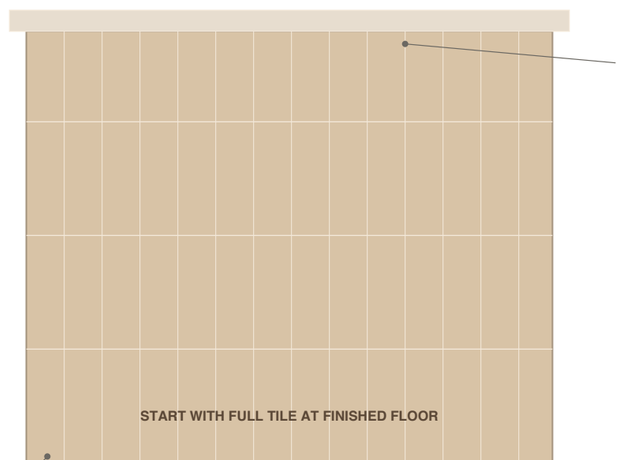

Cut top course to sit beneath counter edge.

Align bottom course level; scribe only if floor is out of level.

4 / MATERIAL & QUANTITY SCHEDULE

Quantities are allowances, not purchase orders

ID	APPLICATION	SPECIFICATION	ALLOWANCE
S-1	Counter + waterfalls	Taj Mahal quartzite; honed finish; 3 cm actual thickness	Fabricator template
T-1	Seating face tile	Edward Martin Natasha 2 x 6 Glossy Porcelain Tile in Canvas	Approx. 25.5 sf net
G-1	Grout	Warm ivory, low contrast; final color by designer sample approval	1/16 in target joint*
C-1	Cabinetry	Existing red lacquer horizontal-pull base cabinets	81 5/8" calc. zone
A-1	Appliance	24 in undercounter wine refrigerator	Exact model TBD

Tile allowance: order 6 boxes (31.92 sf at 5.32 sf/box), providing about 25% over the schematic net face for cuts, shade selection and attic stock. Confirm current packaging before purchase. *Joint width subject to tile calibration and manufacturer guidance.

5 / COORDINATION NOTES

Read before pricing or fabrication

1. Field verify floor level, finished island footprint, existing cabinet widths/heights and adjacent clearances.
2. Maintain 36 in overall finished height, including the 1 3/16 in design top thickness.
3. Taj Mahal is natural quartzite. Designer to approve the exact slabs, face, vein direction, color range and scaled cutting layout before fabrication.
4. Waterfall seams: tight miter with stone-matched epoxy; prioritize vein continuity and coordinate floor scribe with fabricator.
5. Wine fridge: manufacturer dimensions govern. Maintain ventilation, door swing, handle clearance and removable access. Locate receptacle where appliance remains serviceable.
6. Concealed steel support is required for the 16" seating overhang unless the selected fabricator provides a stamped alternative. Support must bear on framing, never on tile/backer.
7. Tile: use a rigid, dimensionally stable substrate suitable for porcelain. Installer to dry-layout from finished floor upward so the only cut horizontal course occurs below the counter.
8. This set conveys design intent and pricing dimensions. Cabinetmaker, fabricator, electrician and installer remain responsible for field conditions, engineering, code compliance and manufacturer requirements.

MATERIAL REFERENCES

Stone: Taj Mahal quartzite, honed, exact slabs by designer approval l Tile: Edward Martin Natasha 2 x 6 Glossy Porcelain Tile in Canvas